



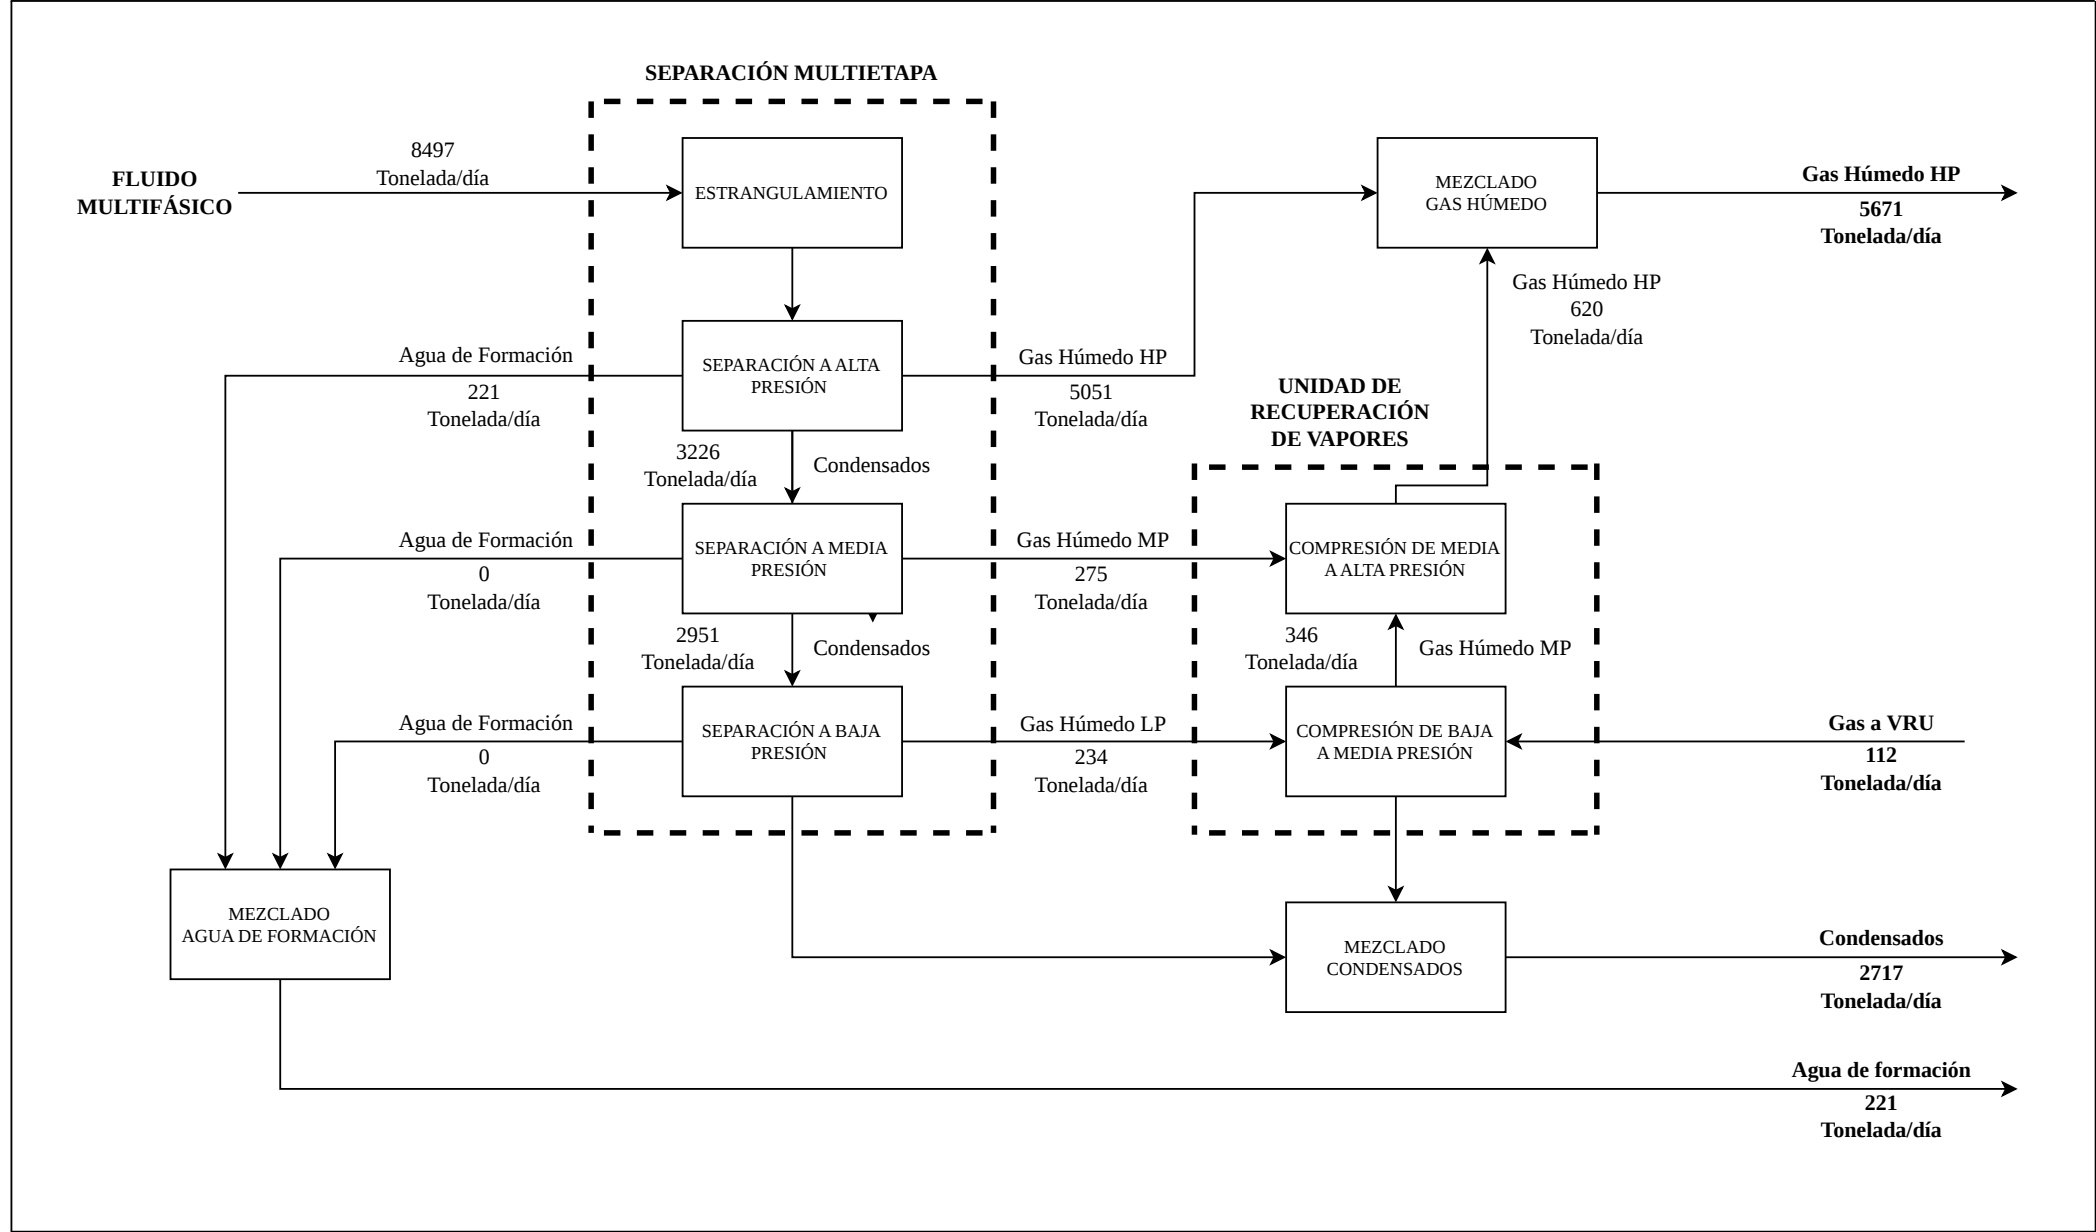

INFORMACIÓN		
DIBUJADO: PALENCIA N.		FECHA: 08/09/2026
REVISADO: ING. PAEZ R. ING. GIRALT J.	APROBADO:	ESCALA: S / E
INTEGRANTES: PALENCIA E. ZIEGLER G. PATERNINA M.		TUTORES ACADÉMICOS: ING. PAEZ R. ING. GIRALT J.

REVISIONES					
Nº	FECHA	DESCRIPCIÓN	ELABORADO POR:	REVISADO POR:	FIRMA
1	08/09/26	Corrección de Balance de Masa	NP	RP	
2					
3					
4					

		
DESCRIPCIÓN: DIAGRAMA DE BLOQUE DE PROCESOS	INSTALACIÓN: DISEÑO DE UNA UNIDAD DE PROCESAMIENTO DE GAS COSTA AFUERA TÍTULO: DBP-01 SEPARACIÓN MULTITETAPA Y RECUPERACIÓN DE VAPORES	HOJA: 1 DE: 3

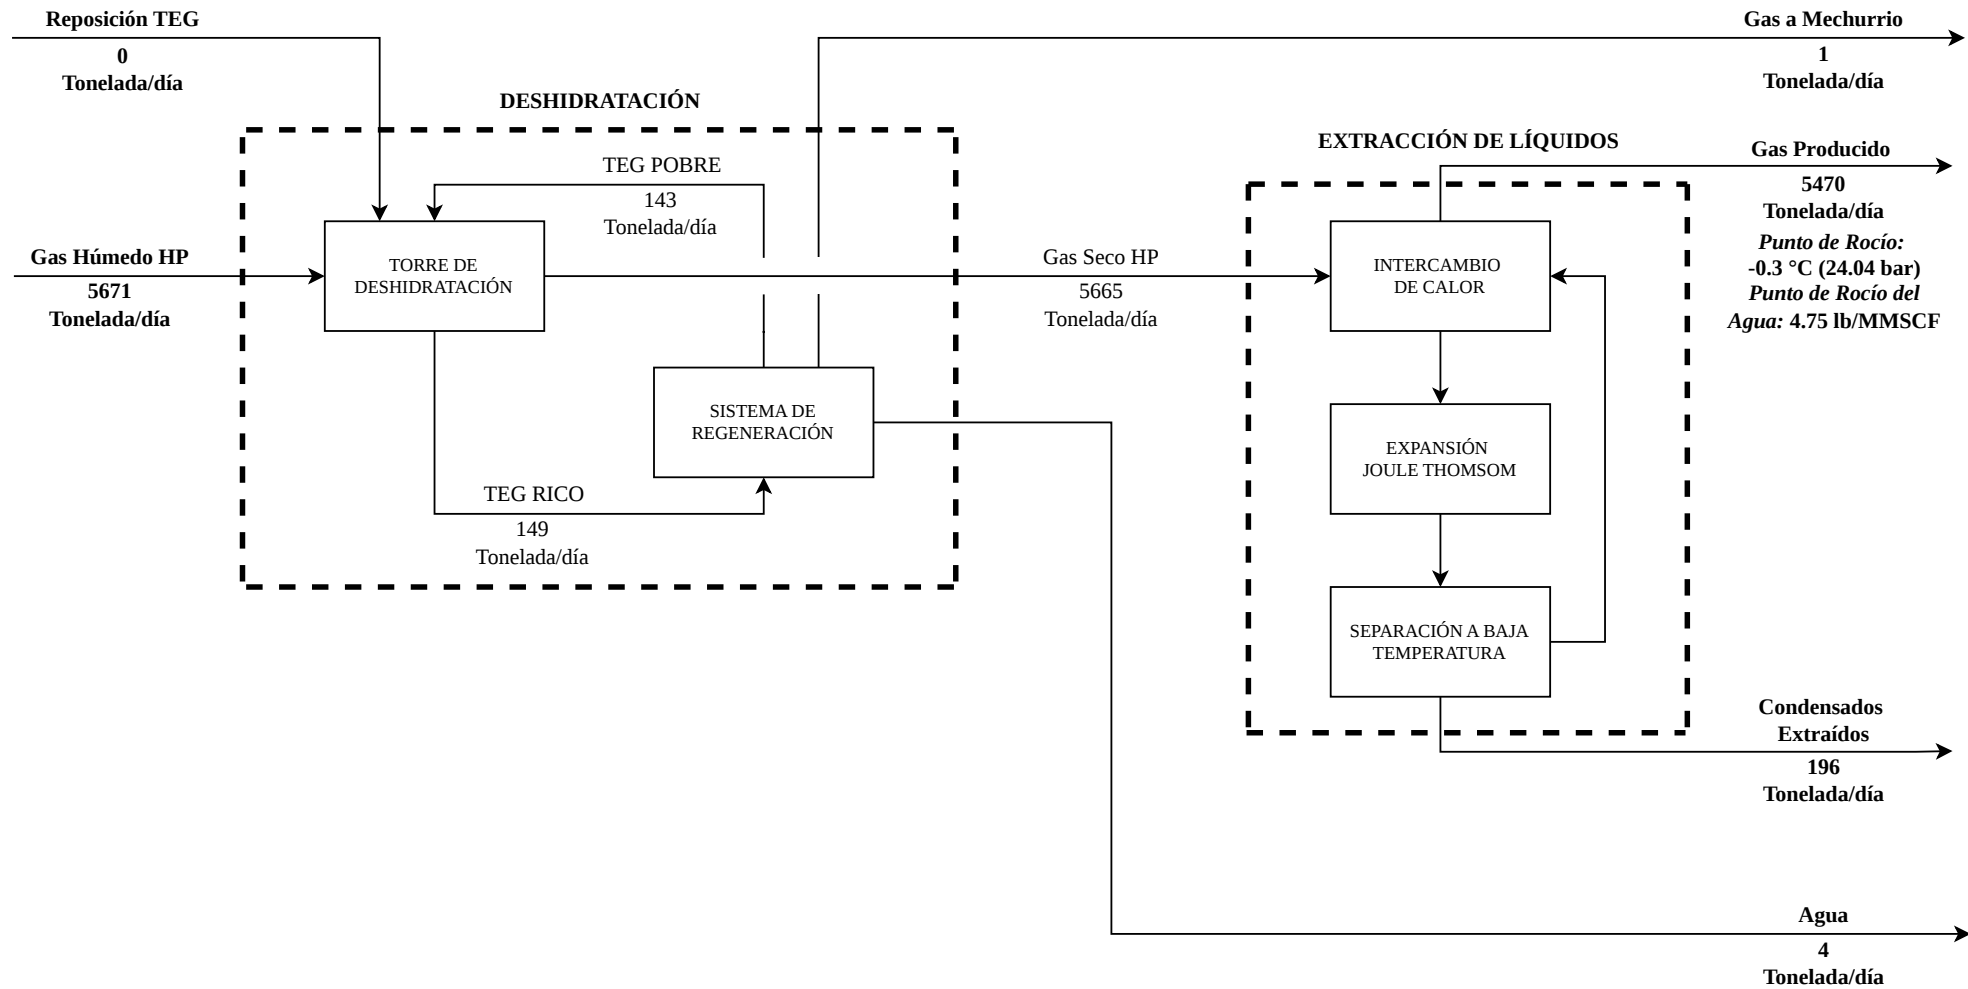

INFORMACIÓN

DIBUJADO: PALENCIA N.	FECHA: 08/09/2026
REVISADO: ING. PAEZ R. ING. GIRALT J.	APROBADO: ESCALA: S / E
INTEGRANTES: PALENCIA E. PATERNINA M.	TUTORES ACADÉMICOS: ING. PAEZ R. ING. GIRALT J.

REVISIONES

Nº	FECHA	DESCRIPCIÓN	ELABORADO POR:	REVISADO POR:	FIRMA
1	08/09/26	Corrección de Balance de Masa	NP	RP	
2					
3					
4					




DESCRIPCIÓN:
DIAGRAMA DE BLOQUE DE PROCESOS



INSTALACIÓN:
DISEÑO DE UNA UNIDAD DE PROCESAMIENTO DE GAS COSTA AFUERA
TÍTULO:
DBP-02
DESHIDRATACIÓN Y EXTRACCIÓN DE LÍQUIDOS




HOJA: 2
DE: 3

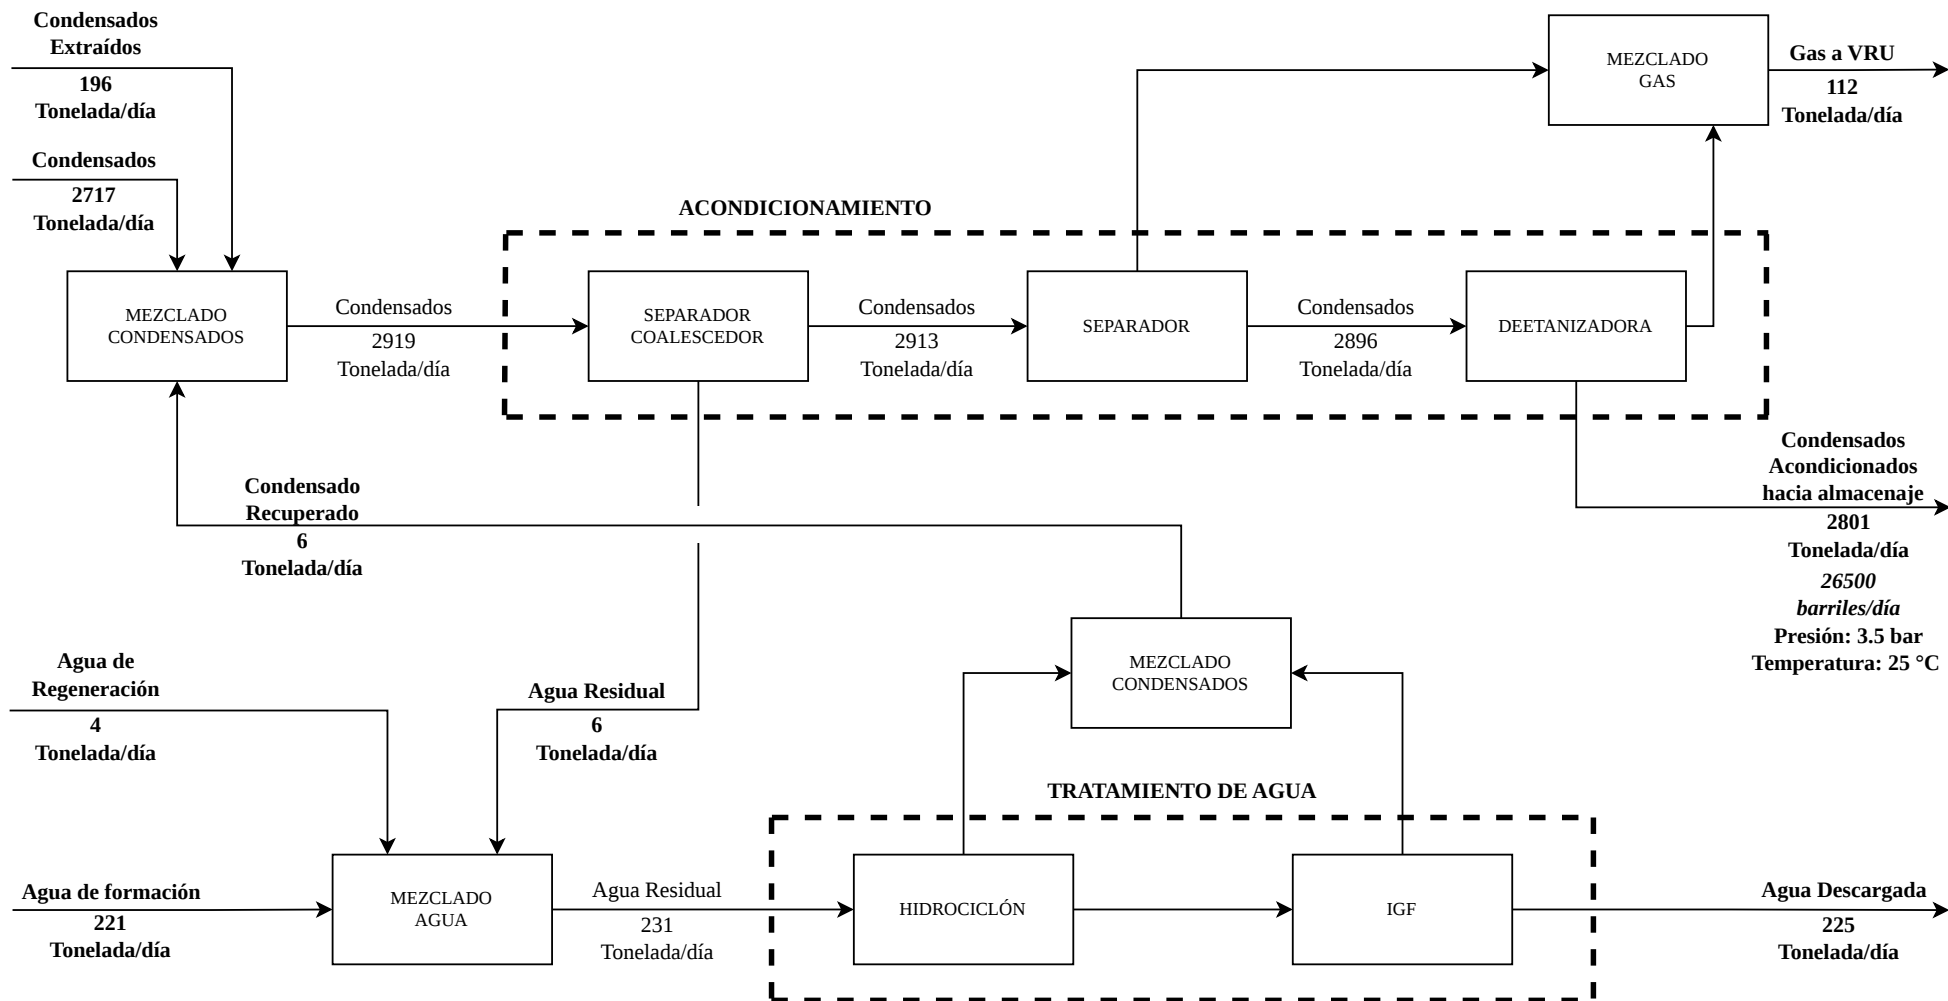

INFORMACIÓN		
DIBUJADO: PALENCIA N.		FECHA: 08/09/2026
REVISADO: ING. PAEZ R. ING. GIRALT J.	APROBADO:	ESCALA: S / E
INTEGRANTES: PALENCIA E. PATERNINA M.	ZIEGLER G.	TUTORES ACADÉMICOS: ING. PAEZ R. ING. GIRALT J.

REVISIONES					
Nº	FECHA	DESCRIPCIÓN	ELABORADO POR:	REVISADO POR:	FIRMA
1	08/09/26	Corrección de Balance de Masa	NP	RP	
2					
3					
4					

		
DESCRIPCIÓN: DIAGRAMA DE BLOQUE DE PROCESOS	INSTALACIÓN: DISEÑO DE UNA UNIDAD DE PROCESAMIENTO DE GAS COSTA AFUERA TÍTULO: DBP-03 ACONDICIONAMIENTO Y TRATAMIENTO DE AGUA	HOJA: 3 DE: 3

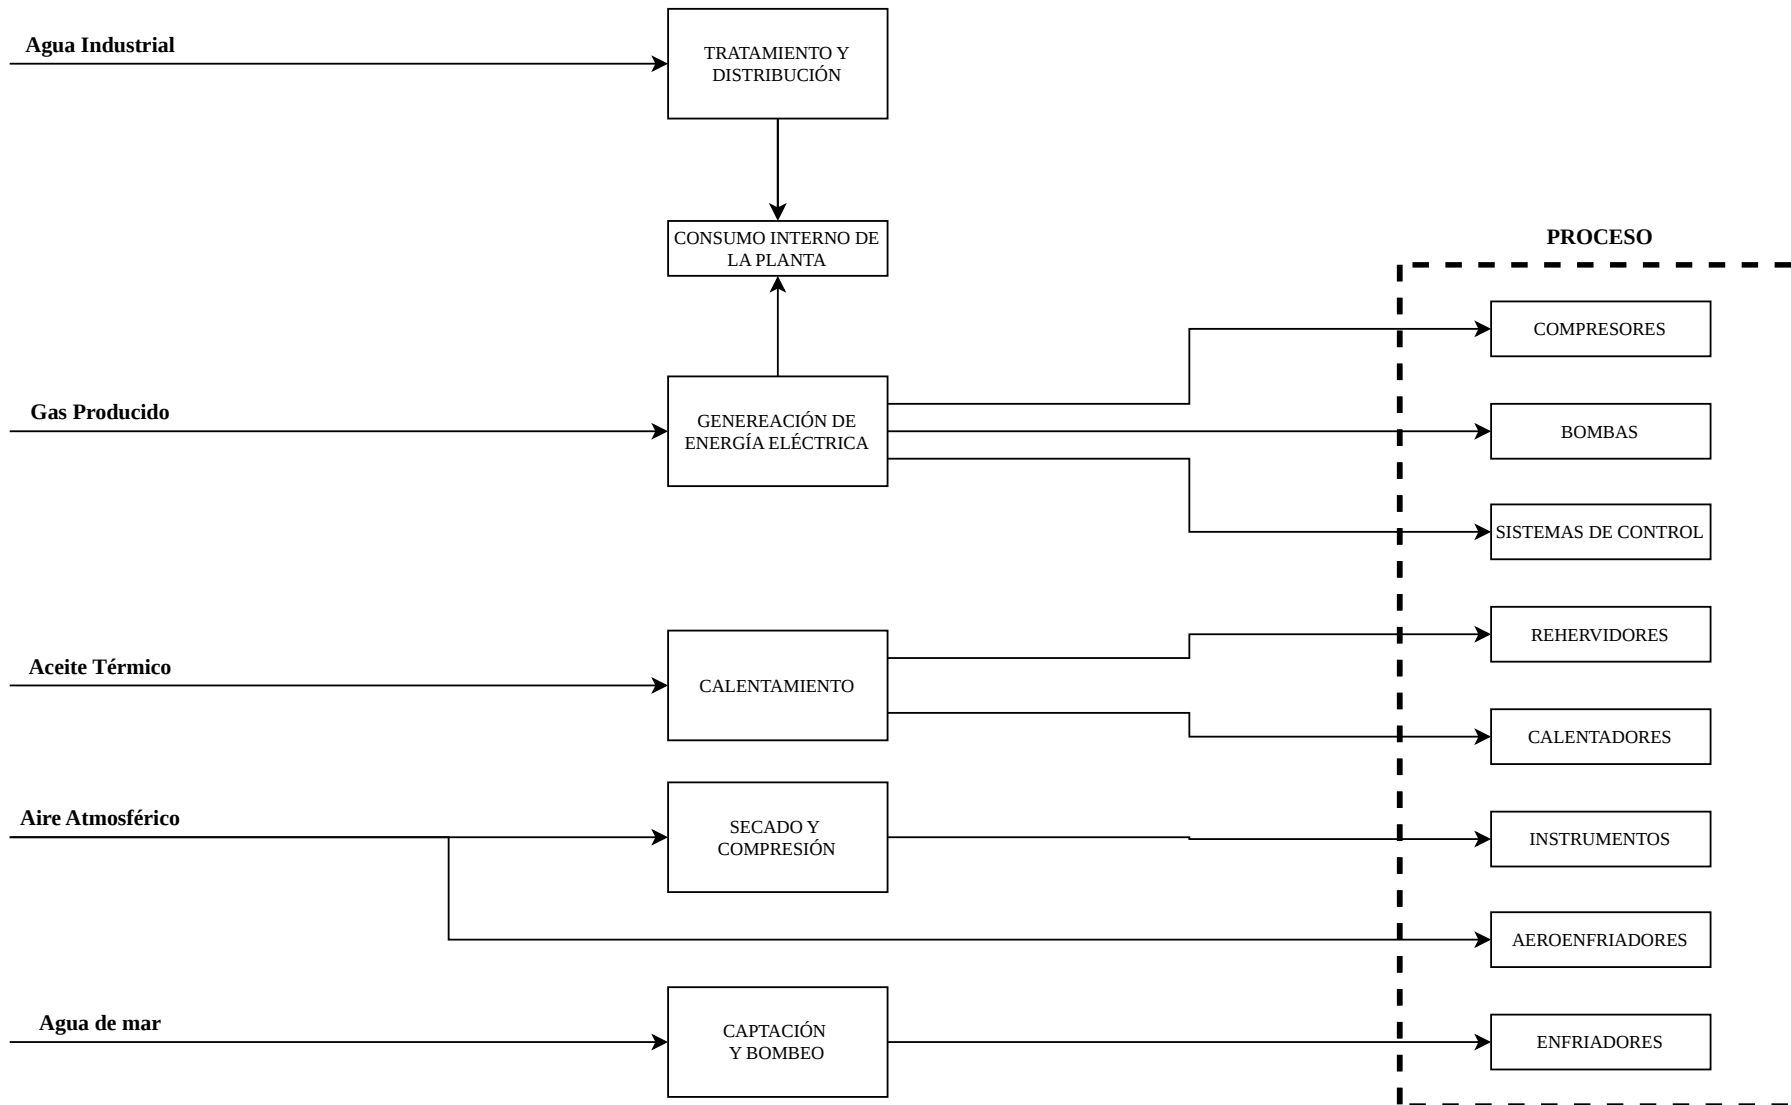

INFORMACIÓN		
DIBUJADO: PALENCIA N.		FECHA: 08/09/2026
REVISADO: ING. PAEZ R. ING. GIRALT J.	APROBADO:	ESCALA: S / E
INTEGRANTES: PALENCIA E. PATERNINA M.	ZIEGLER G.	TUTORES ACADÉMICOS: ING. PAEZ R. ING. GIRALT J.

REVISIONES					
Nº	FECHA	DESCRIPCIÓN	ELABORADO POR:	REVISADO POR:	FIRMA
1	08/09/26	Se agregó agua potable	NP	RP	
2					
3					
4					

 GMN ATLANTIC ENERGY SOLUTIONS		
DESCRIPCIÓN: DIAGRAMA DE BLOQUES DE SERVICIOS	INSTALACIÓN: DISEÑO DE UNA UNIDAD DE PROCESAMIENTO DE GAS COSTA AFUERA TÍTULO: DBS-01 SERVICIOS AUXILIARES	HOJA: 1 DE: 1