


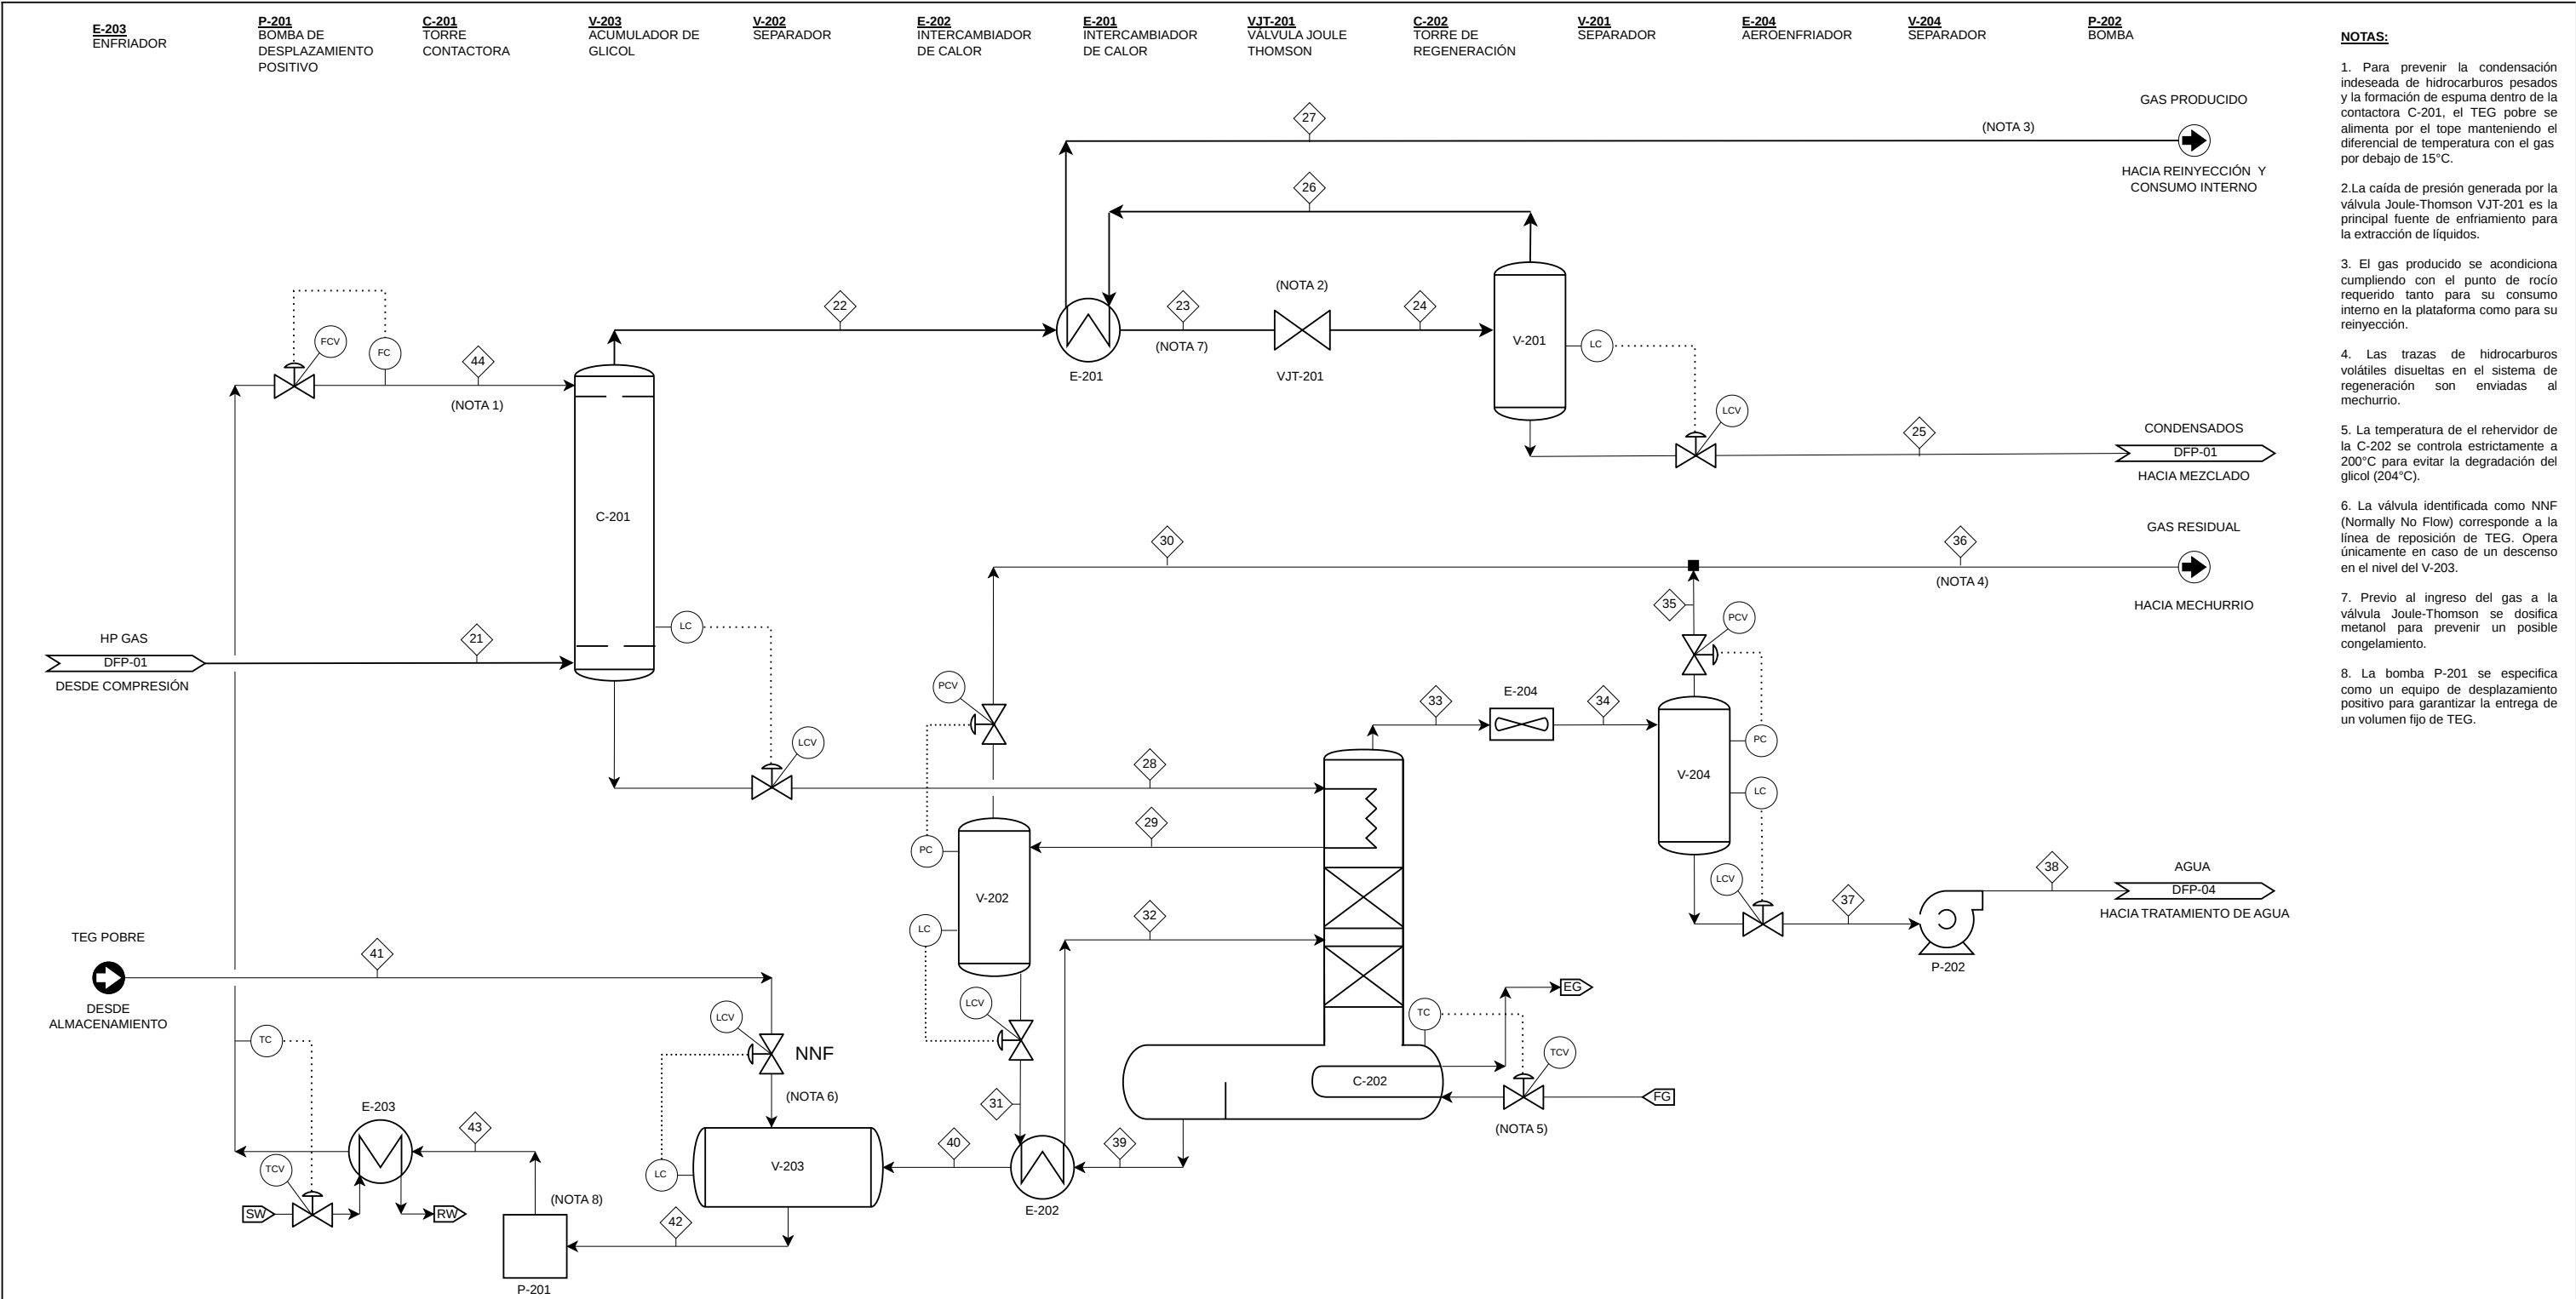


Corriente		21	22	23	24	25	26	27	28	29	30	31	32	33	34	35	36	37	38	39	40	41	42	43	44
Fase		Gaseoso	Gaseoso	Gaseoso	Mezcla	Líquido	Gaseoso	Gaseoso	Líquido	Mezcla	Gaseoso	Líquido	Líquido	Gaseoso	Mezcla	Gaseoso	Gaseoso	Líquido	Líquido	Líquido	Líquido	Líquido	Líquido	Líquido	Líquido
Descripción	Unit	HP gas hacia deshidratación	Gas seco hacia intercambiador Gas-Gas	Gas hacia válvula Joule-Thomson	Mezcla hacia separador	Condensados hacia Acondicionamiento	Gas hacia intercambiador Gas-Gas	Gas Producido hacia reinyección	TEG desde torre de deshidratación	TEG hacia separador	Gas hacia mechorrio	TEG hacia intercambiador	TEG hacia torre de regeneración	Vapor de agua hacia enfriamiento	Mezcla hacia separador	Gas hacia mechorrio	Gas hacia mechorrio	Agua hacia bombeo	Agua hacia tratamiento de agua	TEG hacia intercambiador	TEG hacia surge drum	TEG para reposición	TEG hacia bombeo	TEG hacia calentador	TEG hacia torre de deshidratación
Temperatura	C	41.0	41.5	25.0	0.0	0.0	0.0	21.3	41.4	47.8	47.8	47.8	123.9	100.0	45.0	45.0	43.4	45.0	45.0	200.0	134.8	57.0	134.8	135.8	50.0
Presión	bar	68.30	67.60	67.20	24.40	24.40	24.40	24.00	67.90	11.40	11.40	11.40	11.20	1.00	0.90	0.90	0.90	0.90	5.20	1.00	1.00	67.90	1.00	67.90	67.90
Flujo Molar	MMSCFD	227.00	227.00	227.00	227.00	3.00	224.00	224.00	1.00	1.00	0.00	1.00	1.00	0.00	0.00	0.00	0.00	0.00	0.00	1.00	1.00	0.00	1.00	1.00	1.00
Flujo Másico	tonne/d	5671	5665	5665	5665	196	5470	5470	149	149	1	148	148	5	5	0	1	4	4	143	143	0	143	143	143
Flujo Volumétrico	barrel/day	103243	103198	103198	103198	2171	101027	101027	843	843	11	832	832	34	34	6	17	28	28	798	798	0	798	798	798
Densidad	kg/m3	67.38	66.36	73.43	25.49	597.68	24.65	21.90	1102.68	753.45	10.16	1097.03	1030.80	0.62	11.90	1.12	0.93	992.39	992.50	966.29	1027.13	1105.90	1027.17	1042.35	1109.34
Viscosidad	cP	0.01	0.01	<empty>	<empty>	0.21	0.01	0.01	13.17	<empty>	0.01	11.73	1.99	0.01	<empty>	0.01	<empty>	0.59	0.59	0.62	1.73	10.83	1.73	1.71	12.75

INFORMACIÓN		
DIBUJADO: PALENCIA N.		FECHA: 25/09/2026
REVISADO: ING. PAEZ R. ING. GIRALT J.	APROBADO:	ESCALA: S / E
INTEGRANTES: PALENCIA E. PATERNINA M.	ZIEGLER G.	TUTORES ACADÉMICOS: ING. PAEZ R. ING. GIRALT J.

REVISIONES					
Nº	FECHA	DESCRIPCIÓN	ELABORADO POR:	REVISADO POR:	FIRMA
A	08/09/26	EMISIÓN INICIAL	NP	RP	
B	14/09/26	INCORPORACIÓN DE COMENTARIOS	NP	RP	
0	25/09/26	EMISIÓN ORIGINAL APROBADA	NP	RP	

DESCRIPCIÓN: DIAGRAMA DE FLUJO DE PROCESOS	INSTALACIÓN: DISEÑO DE UNA UNIDAD DE PROCESAMIENTO DE GAS COSTA AFUERA TÍTULO: DFP-02 DESHIDRATACIÓN DEL GAS Y EXTRACCIÓN DE LÍQUIDOS	HOJA: 2 DE: 4

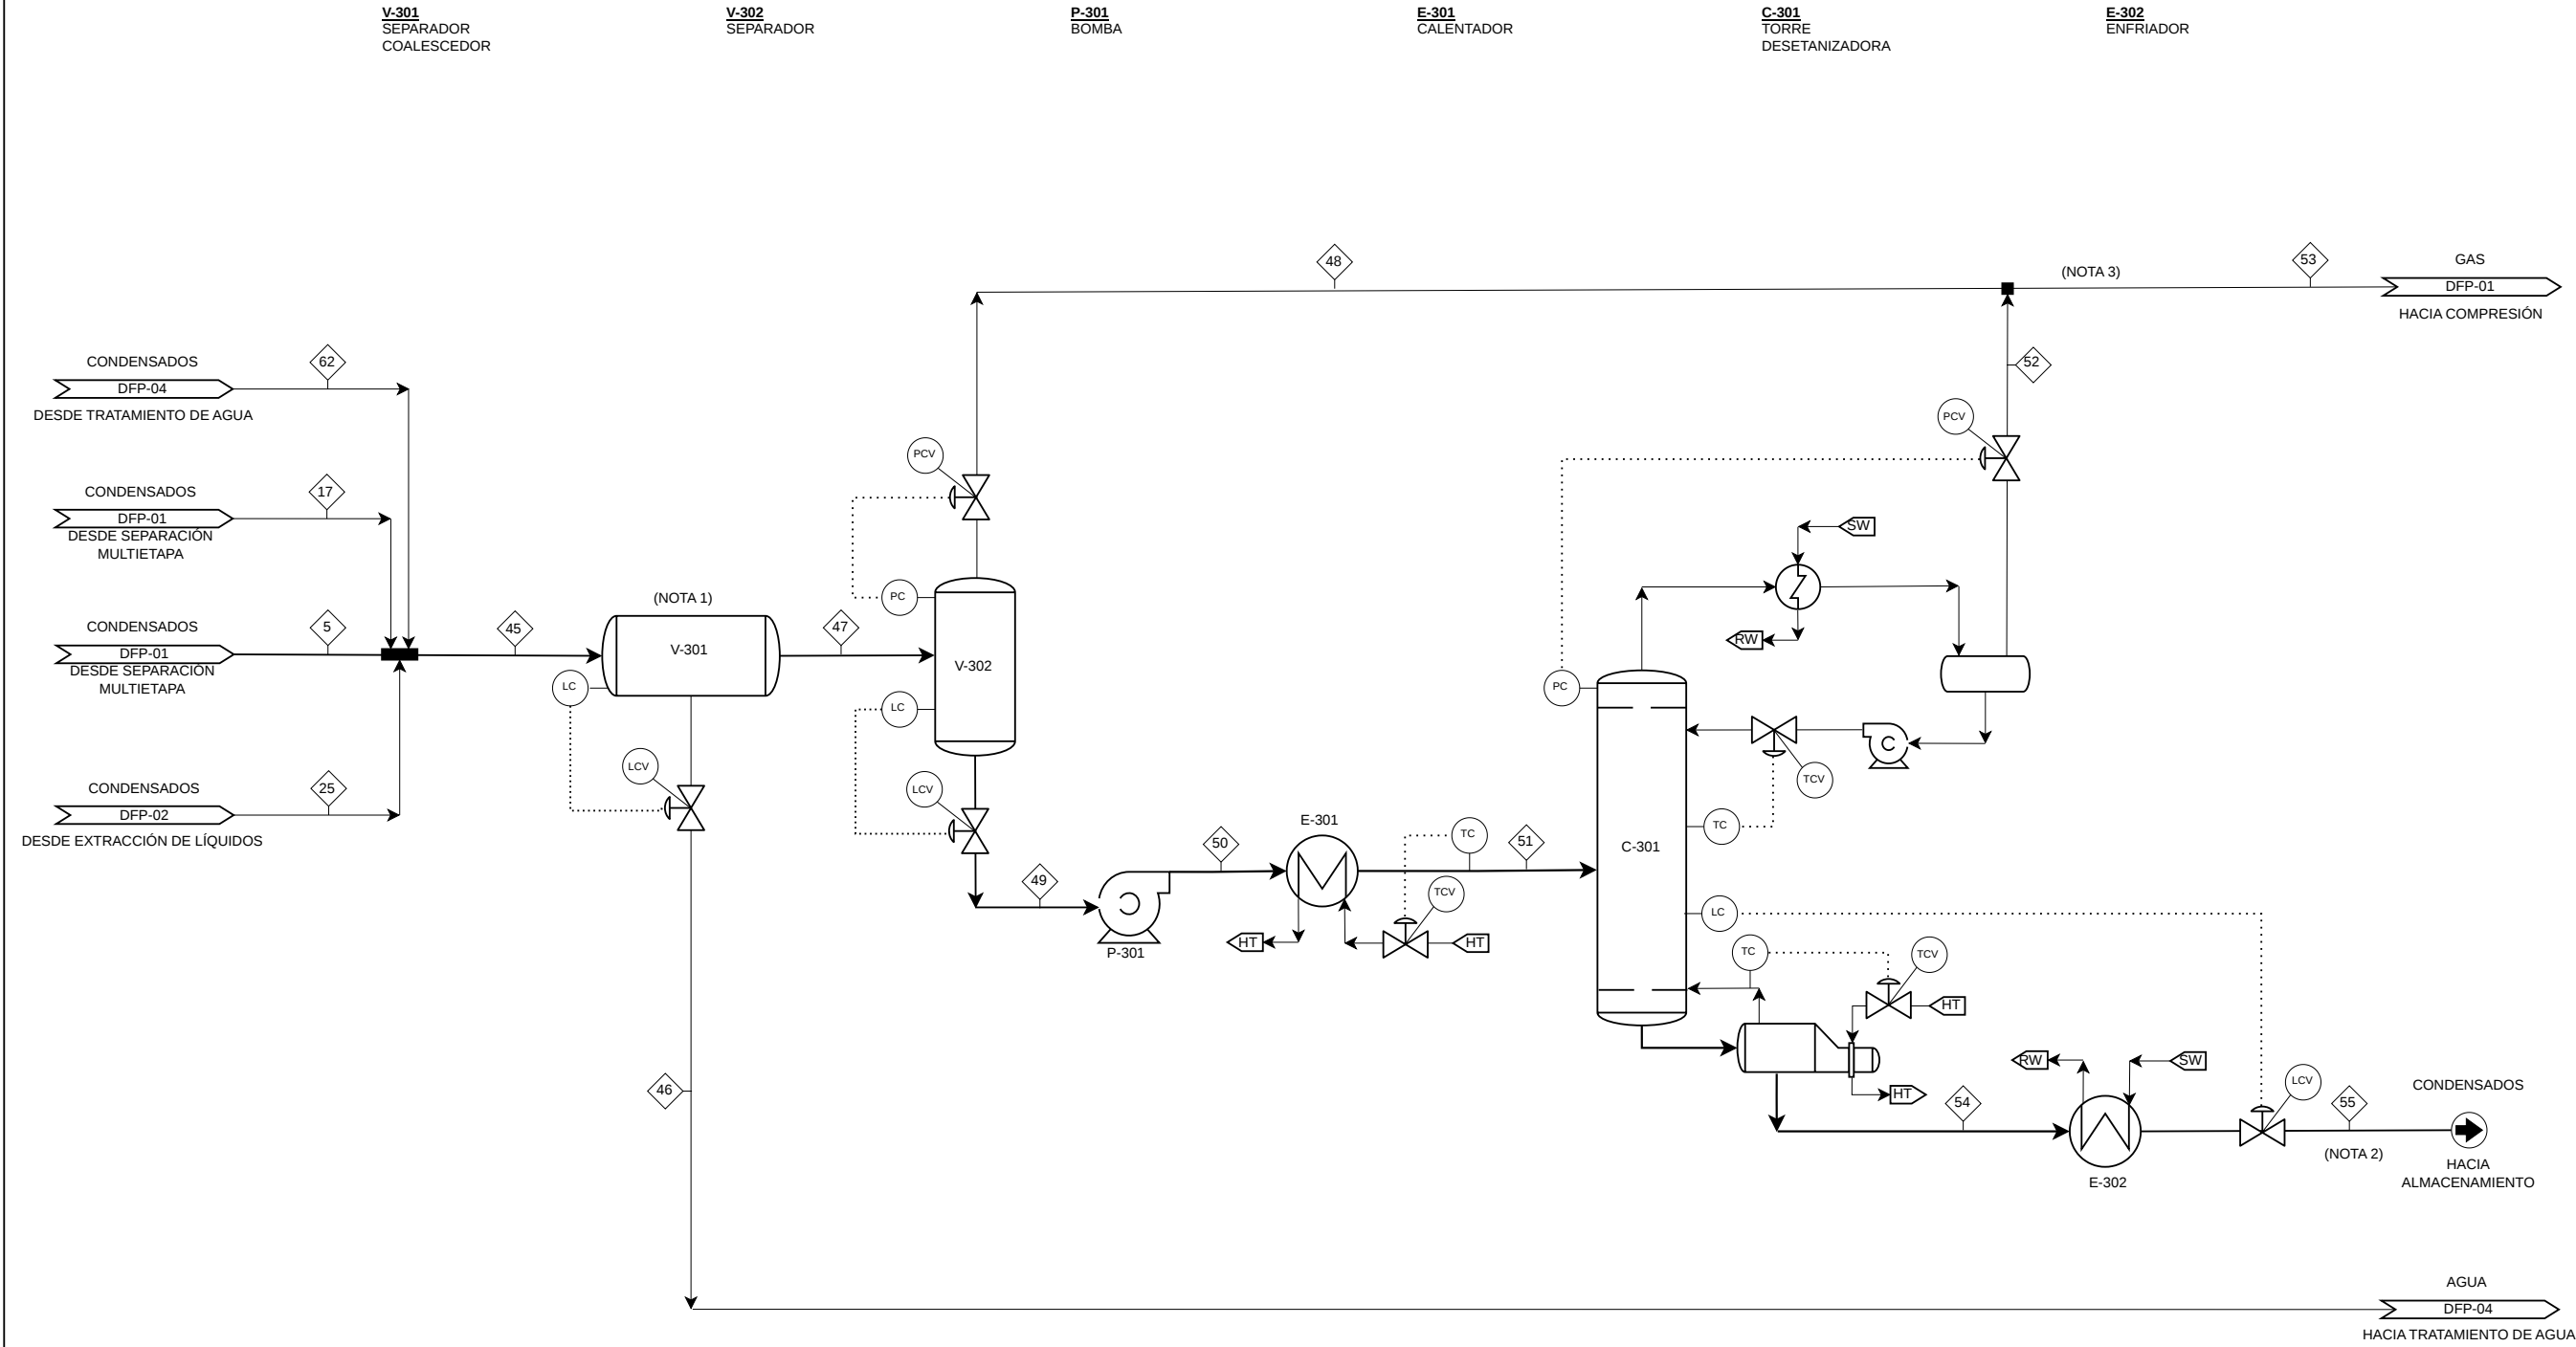


- NOTAS:**
- Previo al ingreso de los condensados a la desetanizadora los condensados pasan por el separador coalescedor para decantar trazas de agua libre emulsionada y prevenir choques térmicos o generación de espuma en la torre.
 - El condensado acondicionado a la salida de la desetanizadora son enviados a almacenamiento en tanques presurizados operando a 4 barg y temperatura atmosférica.
 - Los hidrocarburos en fase gaseosa recuperados del proceso de acondicionamiento son enviados al sistema de recuperación de vapores.

Corriente		5	17	25	62	45	46	47	48	49	50	51	52	53	54	55
Fase		Líquido	Líquido	Líquido	Líquido	Mezcla	Líquido	Mezcla	Gaseoso	Líquido	Líquido	Líquido	Gaseoso	Gaseoso	Mezcla	Líquido
Descripción	Unit	Condensados hacia Acondicionamiento	Condensados interetapa a mezclado	Condensados hacia Acondicionamiento	Condensados hacia Acondicionamiento	Condensados a Acondicionamiento	Agua hacia tratamiento de agua	Condensados hacia separador	Gas hacia compresión	Condensados hacia bombeo	Condensados hacia calentamiento	Condensados hacia Desetanizadora	Gas hacia compresión	Gas hacia compresión	Condensados hacia enfriamiento	Condensados hacia almacenamiento
Temperatura	C	15.2	45.0	0.0	26.6	13.0	4.6	4.6	4.6	4.6	5.6	20.0	25.4	-3.4	195.5	25.0
Presión	bar	5.50	26.90	24.40	6.20	5.50	5.20	5.20	5.20	5.20	27.90	27.90	26.50	5.20	27.20	3.50
Flujo Molar	MMSCFD	26.00	0.00	3.00	0.00	29.00	0.00	29.00	0.00	28.00	28.00	28.00	3.00	3.00	26.00	26.00
Flujo Másico	tonne/d	2717	0	196	0	2913	0	2913	16	2896	2896	2896	95	112	2801	2801
Flujo Volumétrico	barrel/day	26104	0	2171	0	28311	0	28275	260	28015	28015	28015	1517	1777	26498	26498
Densidad	kg/m3	670.12	526.63	597.68	1120.62	384.48	1134.19	425.58	6.28	676.18	677.48	663.91	45.67	7.50	439.81	666.20
Viscosidad	cP	0.39	0.12	0.21	26.76	<empty>	72.85	<empty>	0.01	0.42	0.42	0.36	<empty>	0.01	<empty>	0.37

INFORMACIÓN		
DIBUJADO: PALENCIA N.		FECHA: 25/09/2026
REVISADO: ING. PAEZ R. ING. GIRALT J.	APROBADO:	ESCALA: S / E
INTEGRANTES: PALENCIA E. PATERNINA M.	ZIEGLER G.	TUTORES ACADÉMICOS: ING. PAEZ R. ING. GIRALT J.

REVISIONES					
Nº	FECHA	DESCRIPCIÓN	ELABORADO POR:	REVISADO POR:	FIRMA
A	08/09/26	EMISIÓN INICIAL	NP	RP	
B	14/09/26	INCORPORACIÓN DE COMENTARIOS	NP	RP	
0	25/09/26	EMISIÓN ORIGINAL APROBADA	NP	RP	

					
DESCRIPCIÓN: DIAGRAMA DE FLUJO DE PROCESOS		INSTALACIÓN: DISEÑO DE UNA UNIDAD DE PROCESAMIENTO DE GAS COSTA AFUERA TÍTULO: DFP-03 ACONDICIONAMIENTO DE CONDENSADOS			HOJA: 3 DE: 4

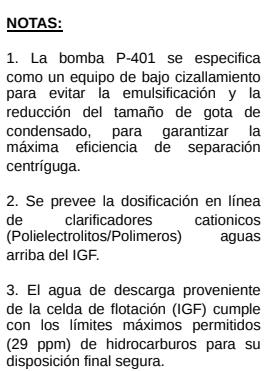

INFORMACIÓN		
DIBUJADO: PALENCIA N.		FECHA: 25/09/2026
REVISADO: ING. PAEZ R. ING. GIRALT J.	APROBADO:	ESCALA: S / E
INTEGRANTES: PALENCIA E. PATERNINA M.	TUTORES ACADÉMICOS: ING. PAEZ R. ING. GIRALT J.	

REVISIONES					
Nº	FECHA	DESCRIPCIÓN	ELABORADO POR:	REVISADO POR:	FIRMA
A	08/09/26	EMISIÓN INICIAL	NP	RP	
B	14/09/26	INCORPORACIÓN DE COMENTARIOS	NP	RP	
0	25/09/26	EMISIÓN ORIGINAL APROBADA	NP	RP	

		
DESCRIPCIÓN: DIAGRAMA DE FLUJO DE PROCESOS	INSTALACIÓN: DISEÑO DE UNA UNIDAD DE PROCESAMIENTO DE GAS COSTA AFUERA TÍTULO: DFP-04 TRATAMIENTO DE AGUA	HOJA: 4 DE: 4