


SEPARACIÓN MULTIETAPA

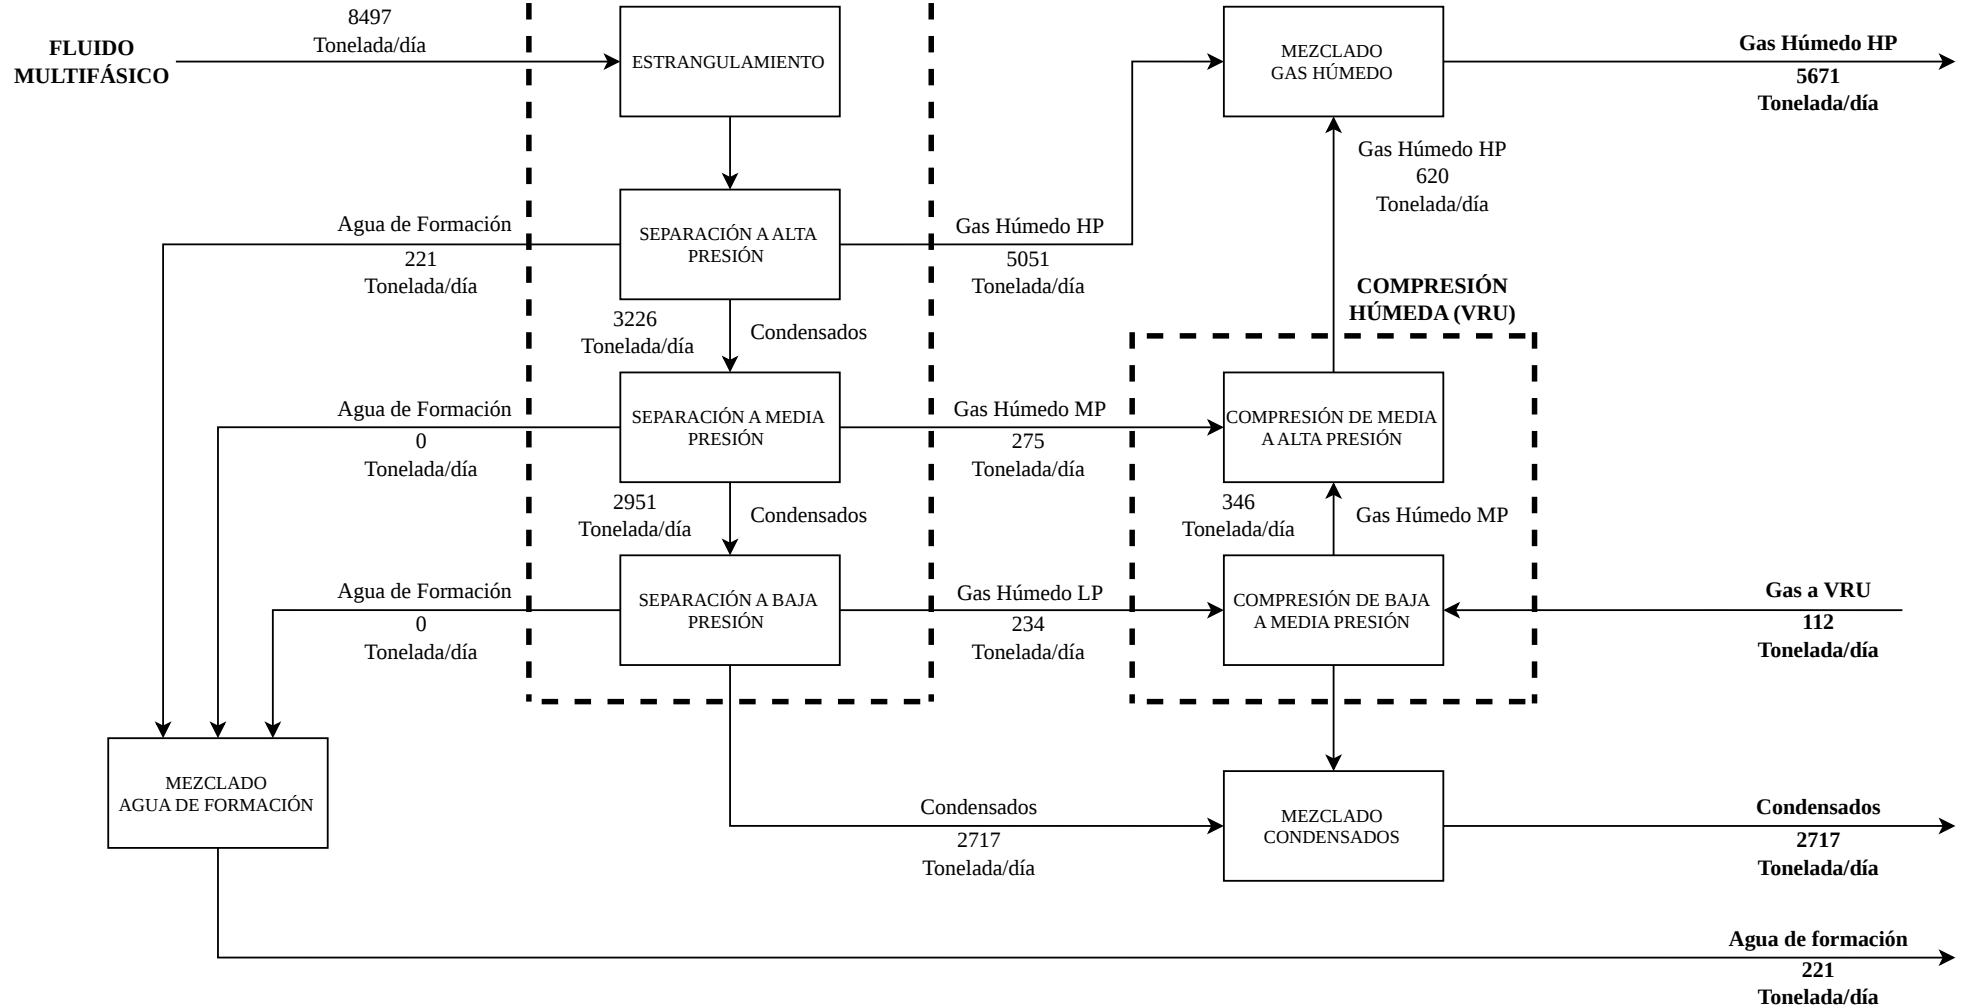


INFORMACIÓN

DIBUJADO: PALENCIA N.	FECHA: 25/09/2026
REVISADO: ING. PAEZ R. ING. GIRALT J.	APROBADO: S / E
INTEGRANTES: PALENCIA E. PATERNINA M.	TUTORES ACADÉMICOS: ING. PAEZ R. ING. GIRALT J.

REVISIONES

Nº	FECHA	DESCRIPCIÓN	ELABORADO POR:	REVISADO POR:	FIRMA
A	08/09/26	EMISIÓN INICIAL	NP	RP	
B	14/09/26	INCORPORACIÓN DE COMENTARIOS	NP	RP	
0	25/09/26	EMISIÓN ORIGINAL APROBADA	NP	RP	

		
DESCRIPCIÓN: DIAGRAMA DE BLOQUE DE PROCESOS	INSTALACIÓN: DISEÑO DE UNA UNIDAD DE PROCESAMIENTO DE GAS COSTA AFUERA TÍTULO: DBP-01 SEPARACIÓN MULTIETAPA Y COMPRESIÓN HÚMEDA	HOJA: 1 DE: 3

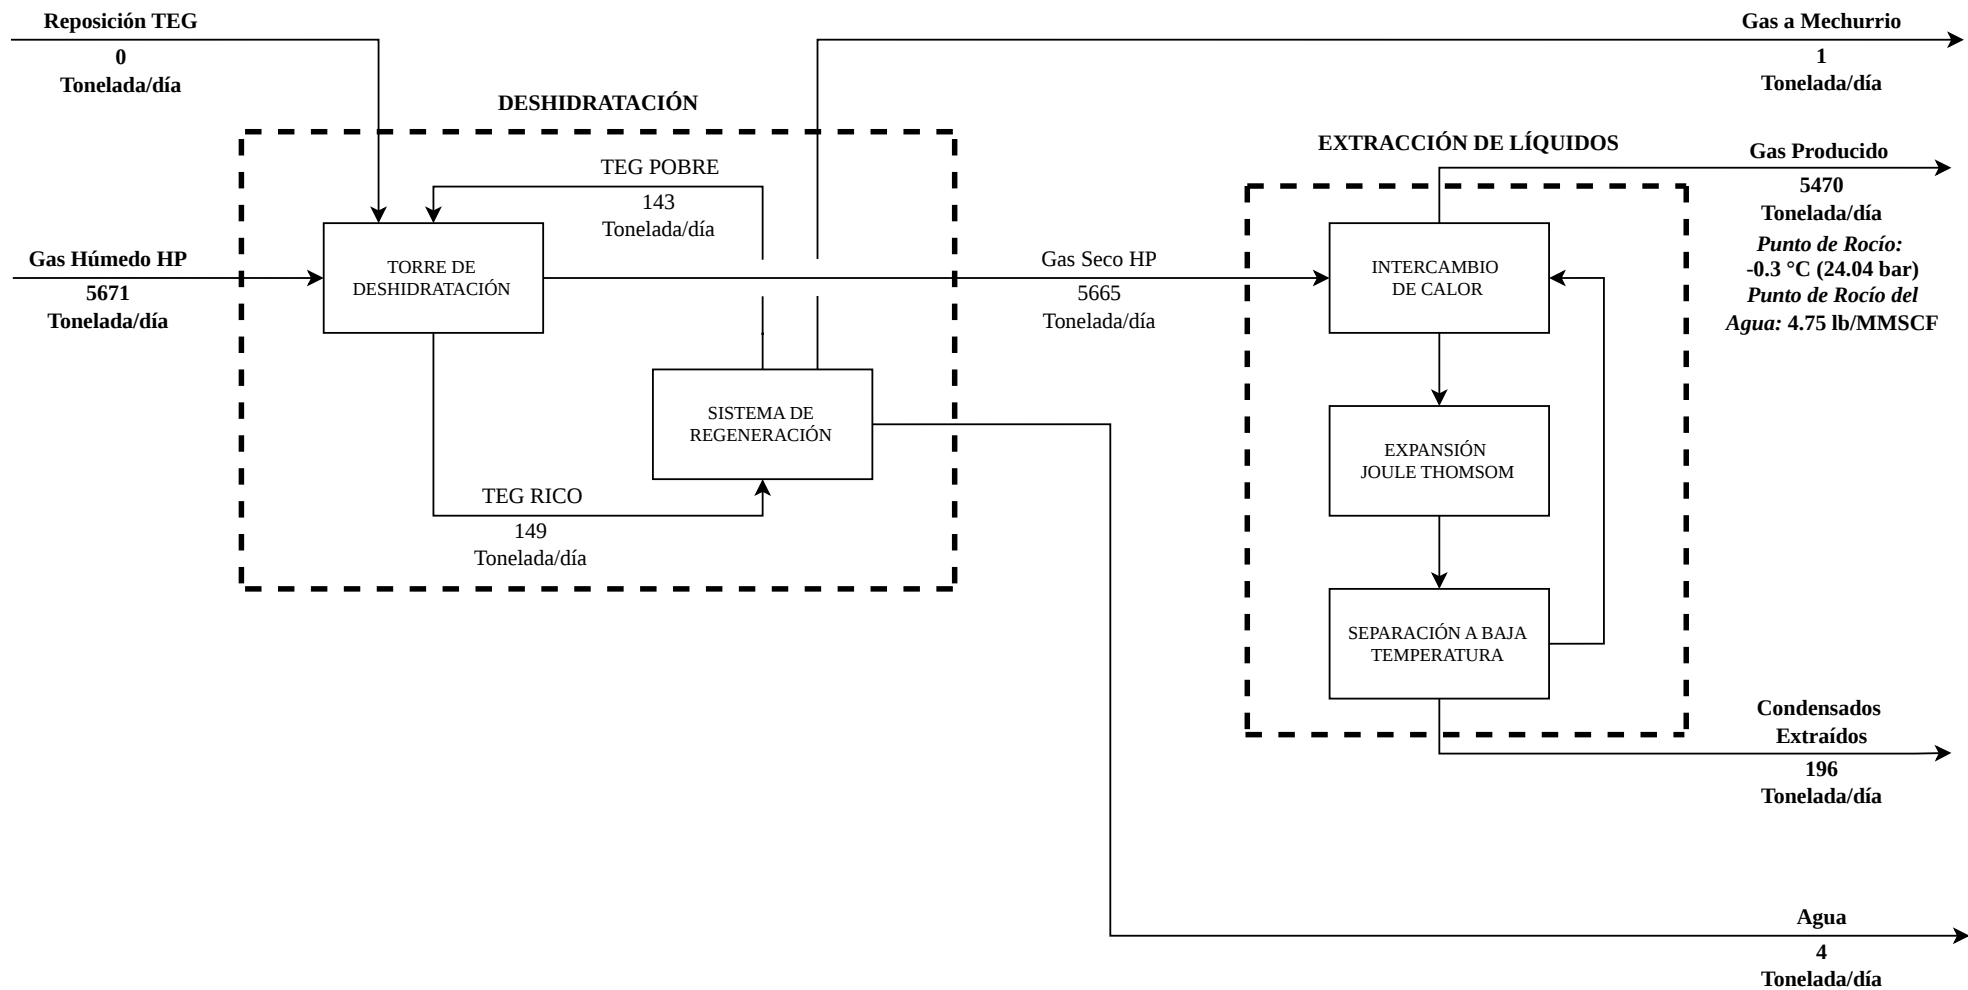

INFORMACIÓN

DIBUJADO: PALENCIA N.	FECHA: 25/09/2026
REVISADO: ING. PAEZ R. ING. GIRALT J.	APROBADO: ING. PAEZ R. ING. GIRALT J.
ING. PAEZ R. ING. GIRALT J.	ESCALA: S / E
ING. PAEZ R. ING. GIRALT J.	TUTORES ACADÉMICOS: ING. PAEZ R. ING. GIRALT J.

REVISIONES

Nº	FECHA	DESCRIPCIÓN	ELABORADO POR:	REVISADO POR:	FIRMA
A	08/09/26	EMISIÓN INICIAL	NP	RP	
B	14/09/26	INCORPORACIÓN DE COMENTARIOS	NP	RP	
0	25/09/26	EMISIÓN ORIGINAL APROBADA	NP	RP	




DESCRIPCIÓN:
DIAGRAMA DE BLOQUE DE
PROCESOS



INSTALACIÓN:
DISEÑO DE UNA UNIDAD DE PROCESAMIENTO DE
GAS COSTA AFUERA
TÍTULO:
DBP-02
DESHIDRATACIÓN Y EXTRACCIÓN DE LÍQUIDOS



HOJA: 2
DE: 3

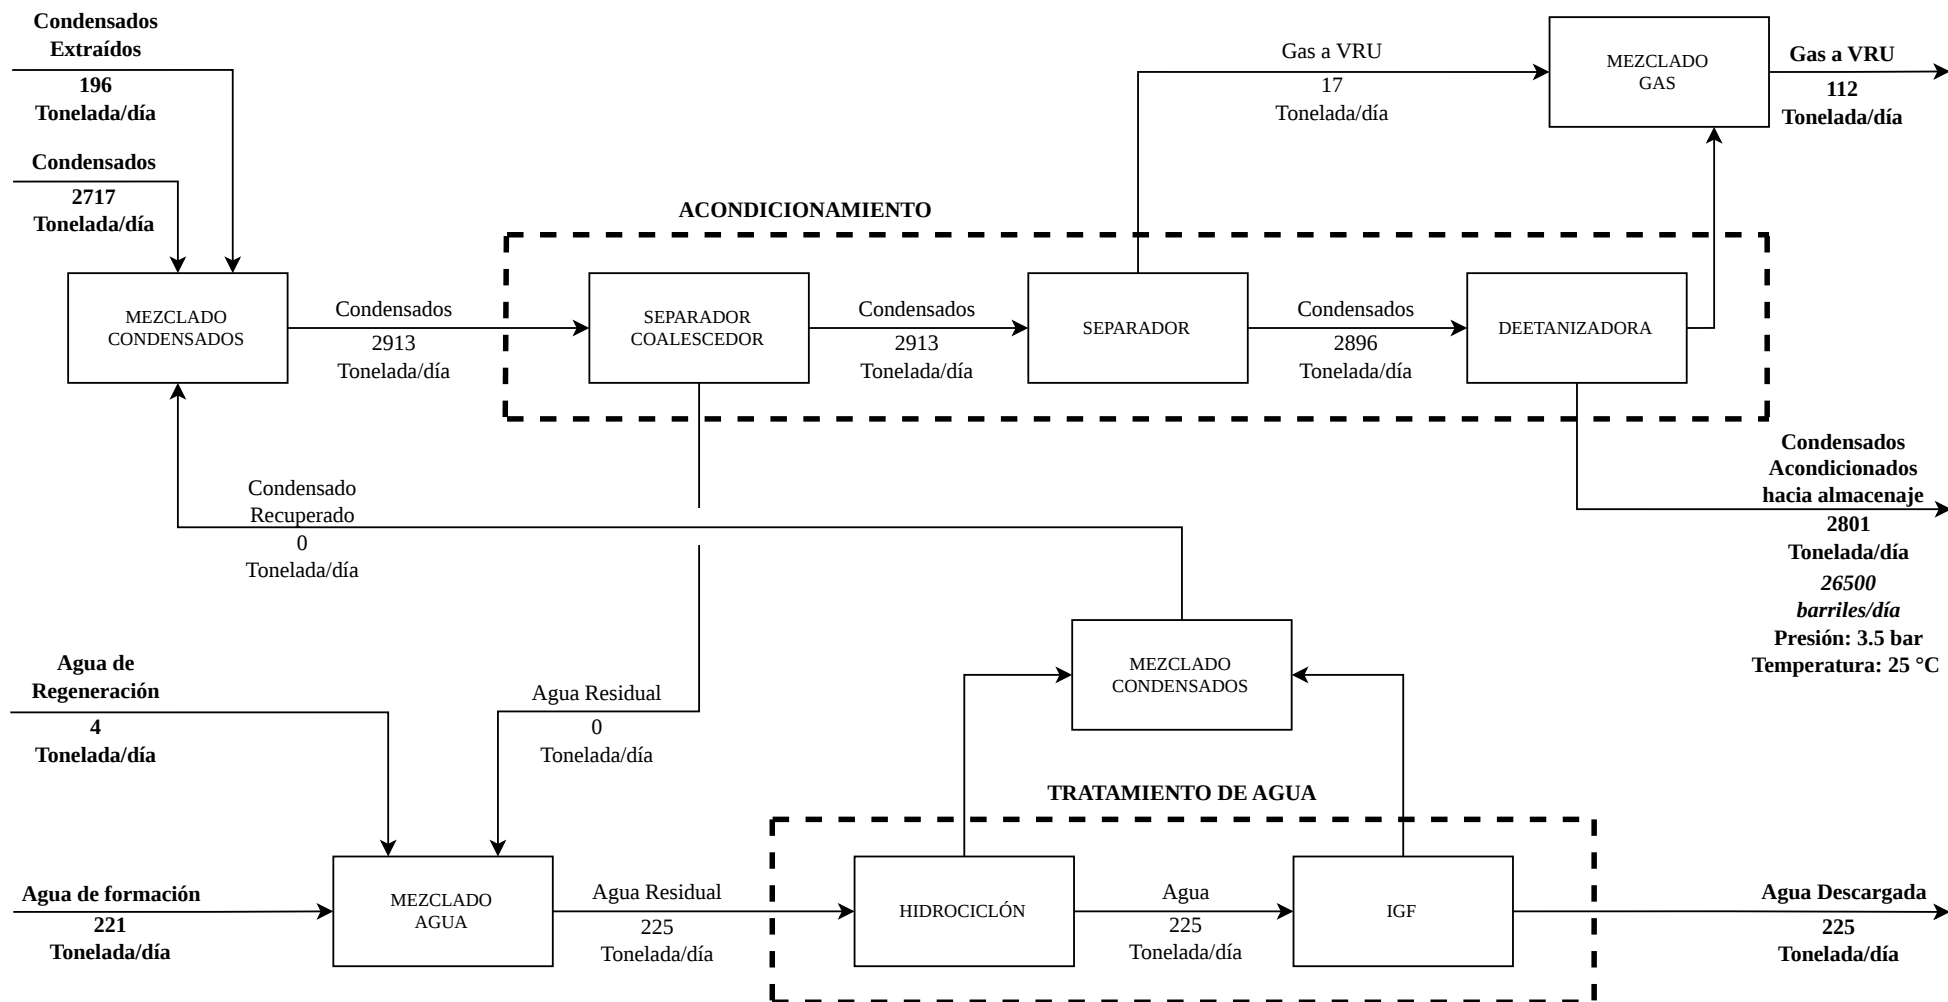

INFORMACIÓN			
DIBUJADO: PALENCIA N.		FECHA: 25/09/2026	
REVISADO: ING. PAEZ R. ING. GIRALT J.	APROBADO:	ESCALA: S / E	
INTEGRANTES: PALENCIA E. PATERNINA M.	ZIEGLER G.	TUTORES ACADÉMICOS: ING. PAEZ R. ING. GIRALT J.	

REVISIONES					
Nº	FECHA	DESCRIPCIÓN	ELABORADO POR:	REVISADO POR:	FIRMA
A	08/09/26	EMISIÓN INICIAL	NP	RP	
B	14/09/26	INCORPORACIÓN DE COMENTARIOS	NP	RP	
0	25/09/26	EMISIÓN ORIGINAL APROBADA	NP	RP	

		
DESCRIPCIÓN: DIAGRAMA DE BLOQUE DE PROCESOS	INSTALACIÓN: DISEÑO DE UNA UNIDAD DE PROCESAMIENTO DE GAS COSTA AFUERA TÍTULO: DBP-03 ACONDICIONAMIENTO Y TRATAMIENTO DE AGUA	HOJA: 3 DE: 3